


Total areas		
 Footprint	1	6,753 SF
 Net area	22	5,962 SF
 Doors area	19	44 SF
 Gross area	20	6,677 SF
 Gross Internal Area	...	206,237 SF
Total lines		
 Doors centerline	19	61 FT
 Wall centerline	133	1,009 FT
 Wall Perimeter	22	1,406 FT
Total counts		
 Toilet	2	2 EA
 Sink	4	4 EA
 Single Swing Door	21	21 EA

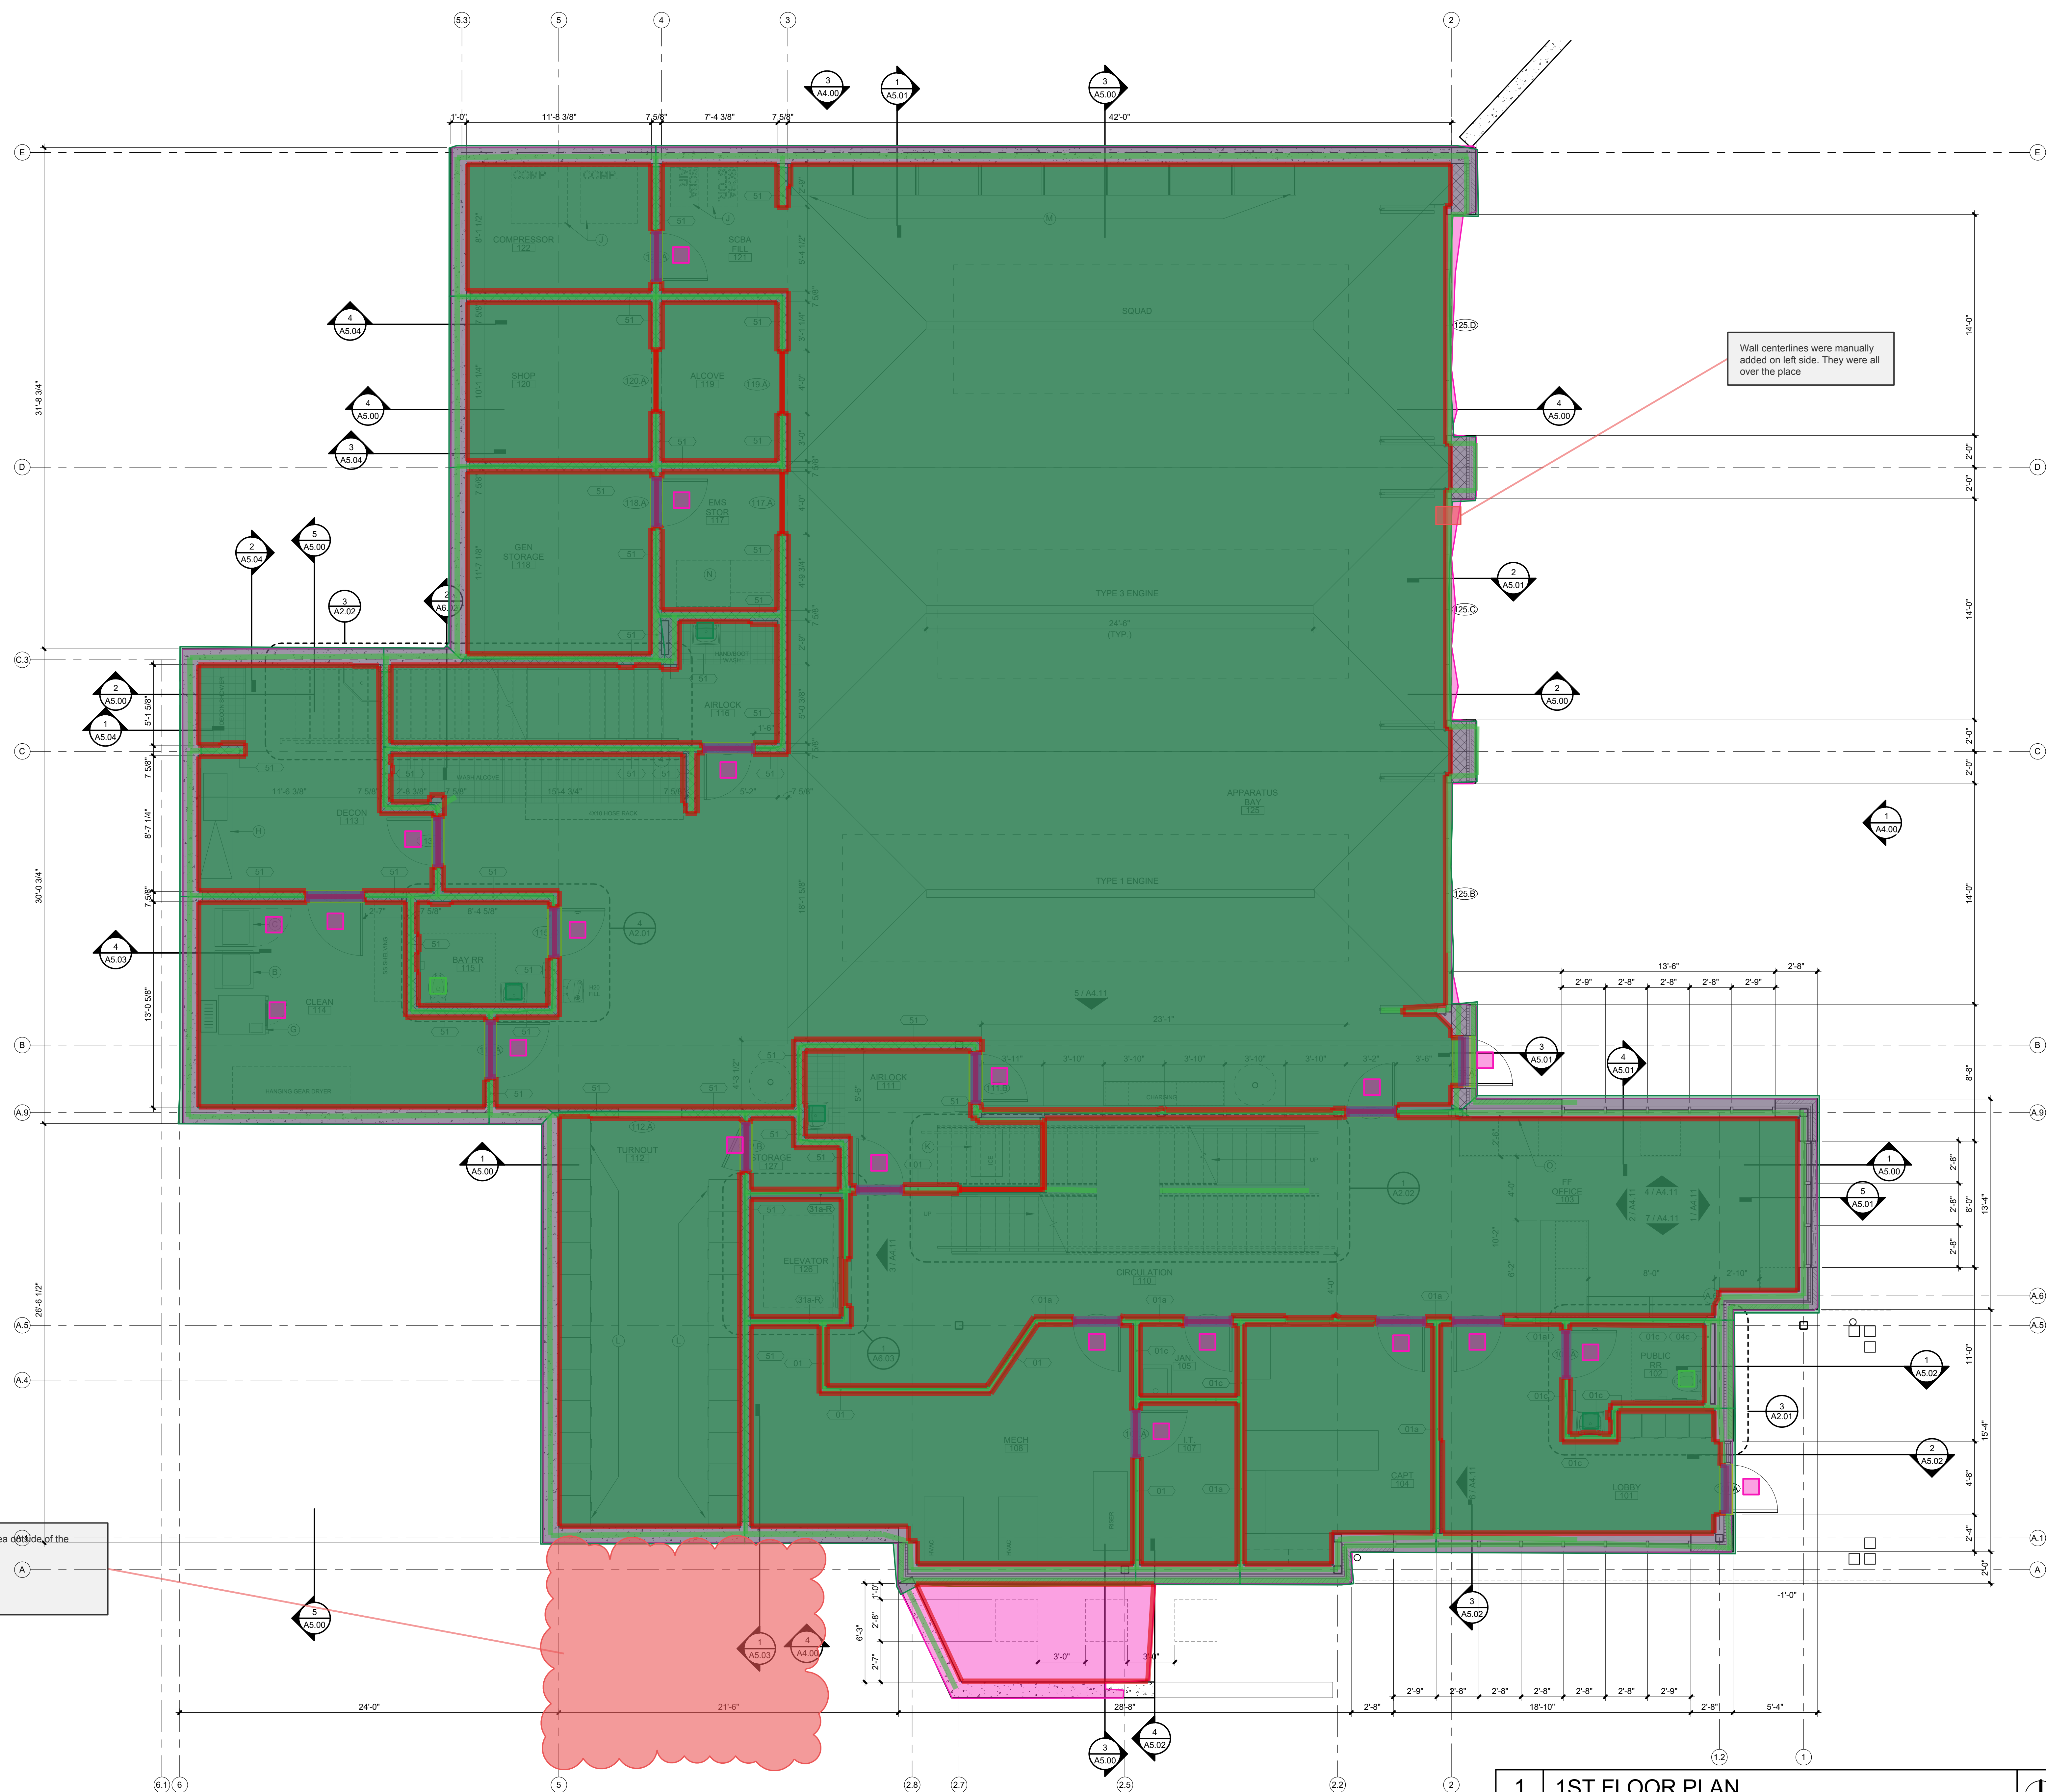

**Olathe Fire
Station No. 8**
14700 Lakeshore Dr
Olathe KS



Project No.:	19003
Date:	02.17.2020
Issued For:	DESIGN DEVELOPMENT

[illegible]

REGISTRATION

NOT FOR CONSTRUCTION

PROJECT TEAM	
ARCHITECT	FINKLE-WILLIAMS ARCHITECTURE
FIRE STATION CONSULTANT	TCA ARCHITECTURE
CIVIL	SK DESIGN GROUP
LANDSCAPE	SWT DESIGN
STRUCTURAL	BOB D. CAMPBELL
PLUMBING	LANKFORD FENDLER
MECHANICAL	LANKFORD FENDLER
ELECTRICAL	LANKFORD FENDLER
CONTRACTOR	TURNER CONSTRUCTION

FINKLE + WILLIAMS
ARCHITECTURE

7007 College Blvd, Suite 411
Overland Park, Kansas 66211
913+498-1550


SHEET TITLE

FIRST FLOOR
PLAN

SHEET NUMBER

A1.01

C:\Users\koster\Documents\Online_FSB-NELV_Central_R18_allenfordster.txt	
---	--

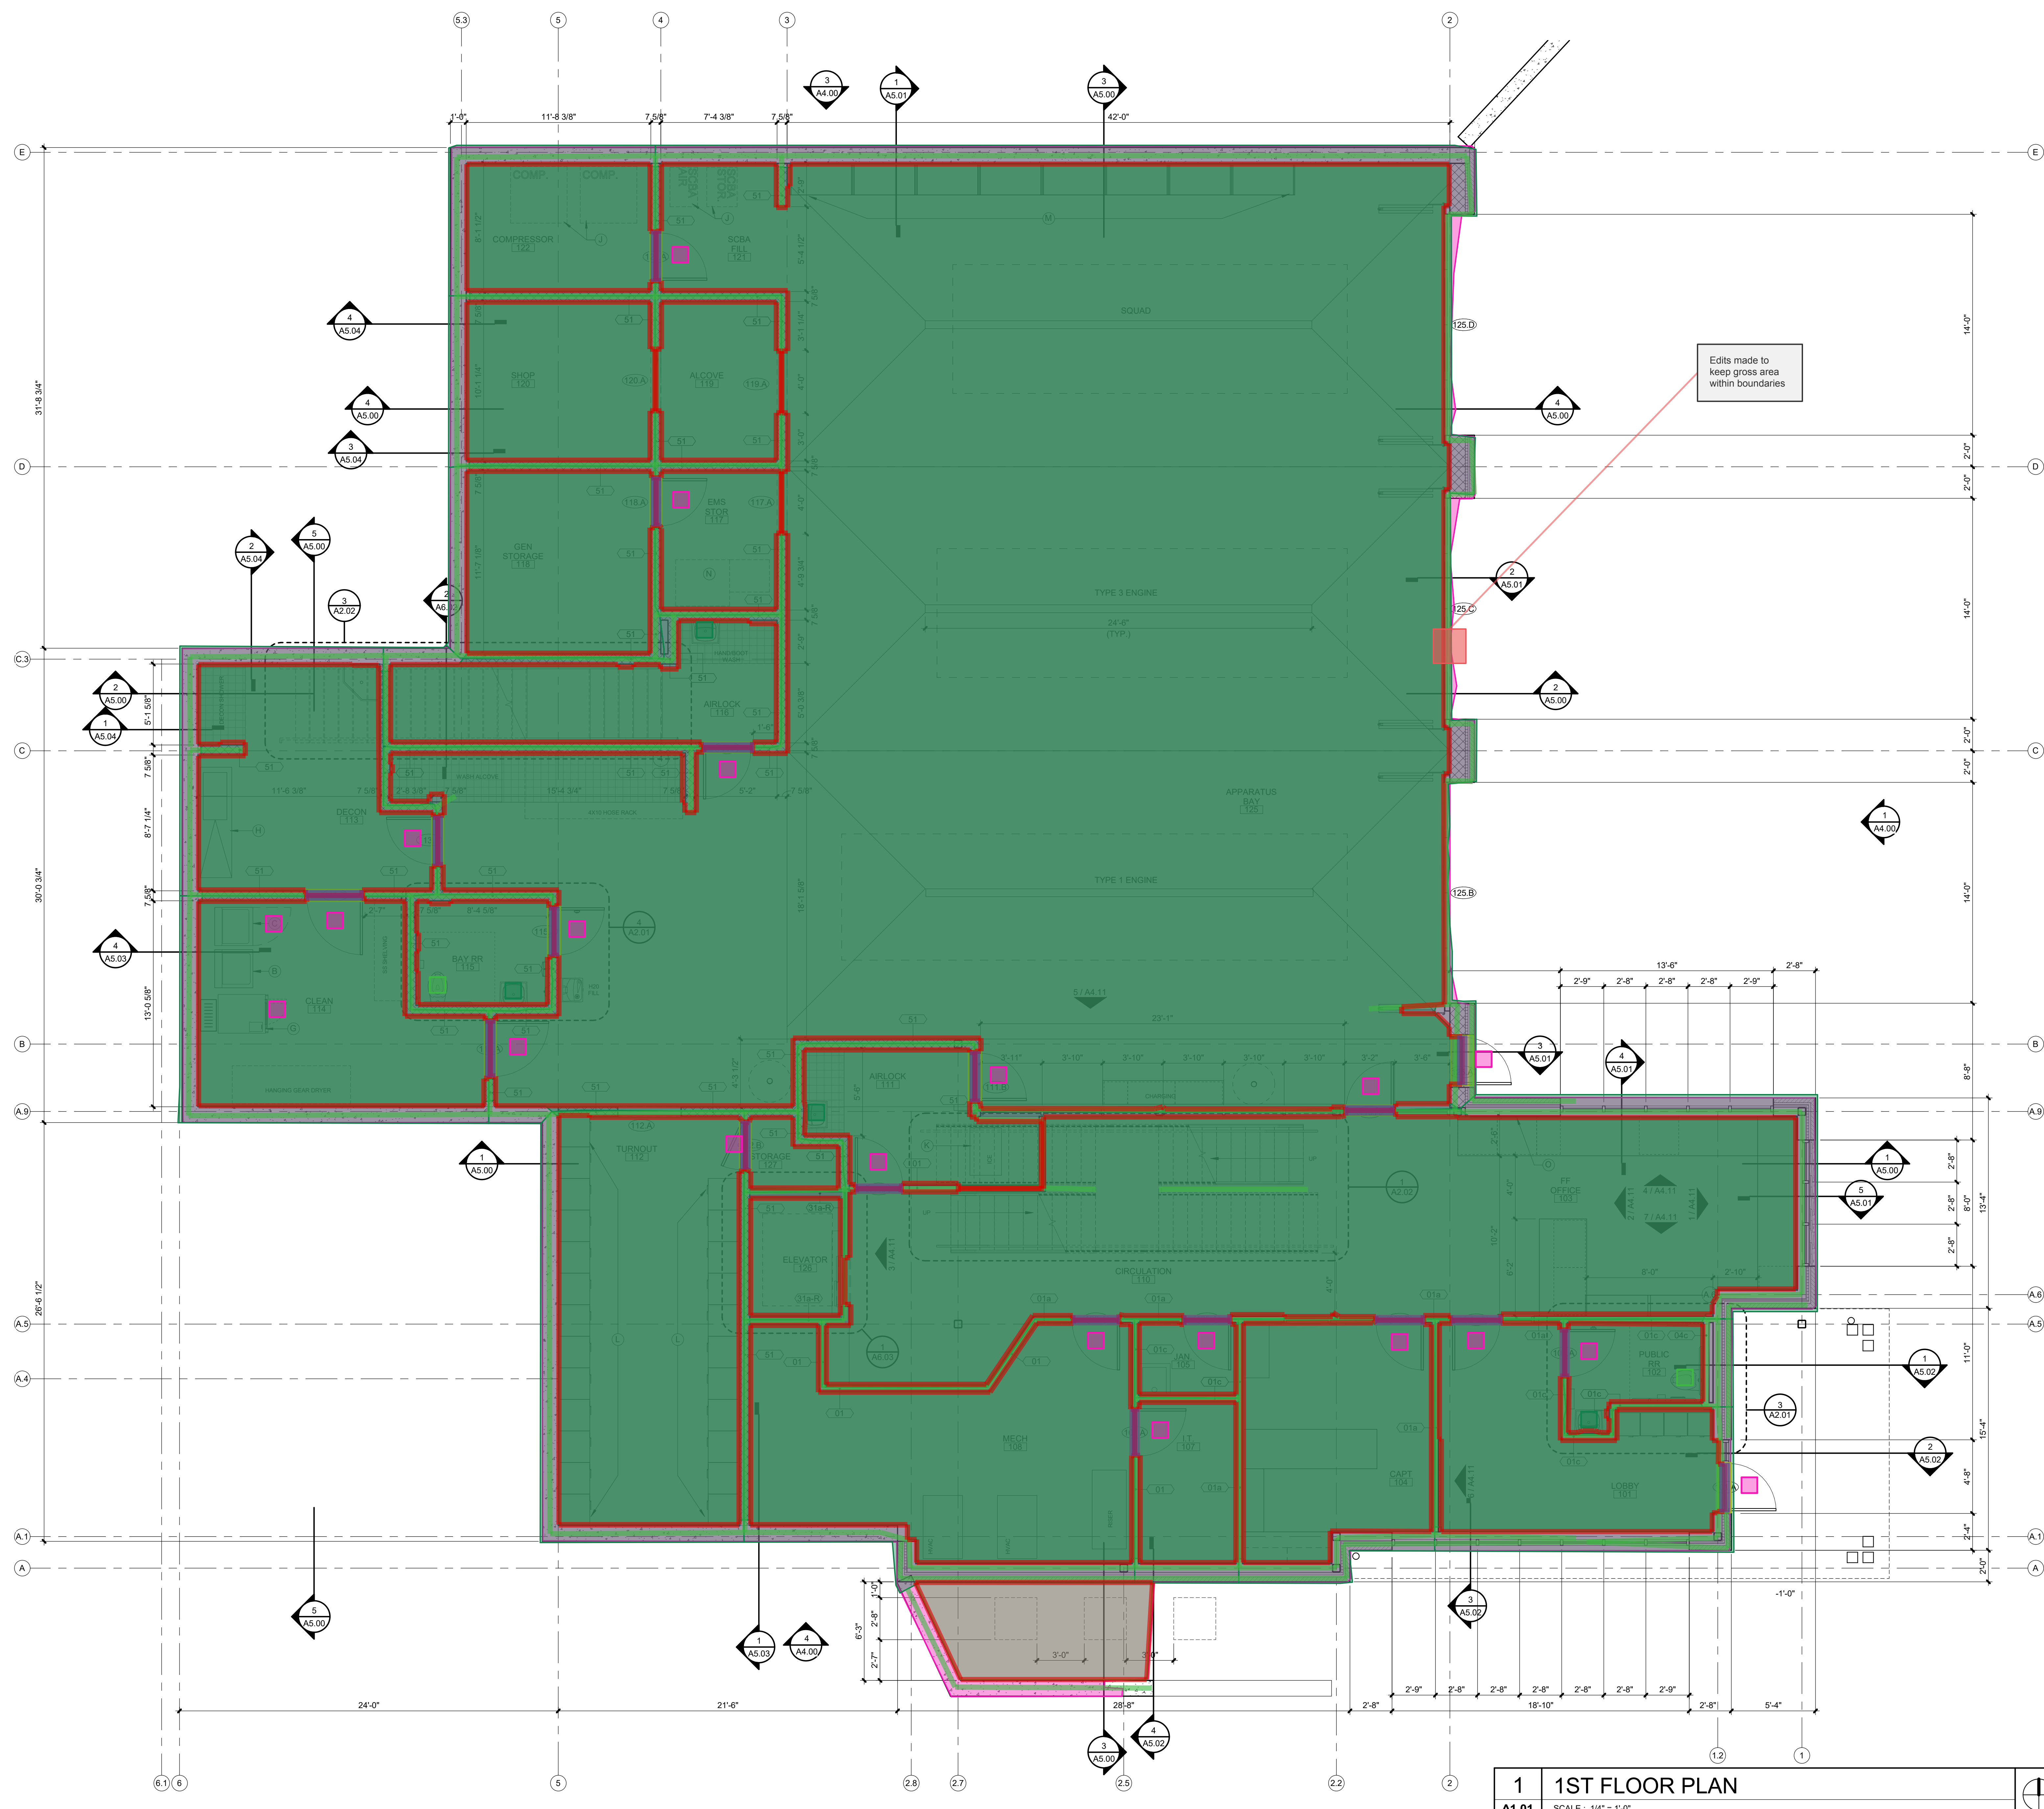

Olathe Fire
Station No. 8
14700 Lakeshore Dr
Olathe KS



Project No.:	19003
Date:	02.17.2020
Issued For:	DESIGN DEVELOPMENT

[illegible]

REGISTRATION

NOT FOR CONSTRUCTION

PROJECT TEAM

ARCHITECT	FINKLE+WILLIAMS ARCHITECTURE
FIRE STATION CONSULTANT	TCA ARCHITECTS
CIVIL	SK DESIGN GROUP
LANDSCAPE	SWT DESIGN
STRUCTURAL	BOB D. CAMPBELL
PLUMBING	LANKFORD FRIEDMAN
MECHANICAL	LANKFORD FRIEDMAN
ELECTRICAL	LANKFORD FRIEDMAN
CONTRACTOR	TURNER CONSTRUCTION

FINKLE + WILLIAMS
ARCHITECTS

7007 College Blvd, Suite
Overland Park, Kansas 66
913+498-1550

SHEET TITLE

FIRST FLOOR
PLAN

SHEET NUMBER

A1.01

C:\Users\efoster\Documents\Olathe FSS-NEW_Central_R18_ellenfoster.nt

C:\Users\kfooster\Documents\Olaith FS8-NEW_Central_R18_ellenfooster.nt