


Togal areas	
Footprint 1	733 SF
Net area 13	617 SF
Doors area 1	1 SF
Gross area 12	664 SF
Gross Internal Area (GIA)	12591 SF
Togal lines	
Doors centerline 1	2 FT
Wall centerline 58	240 FT
Wall Perimeter 14	385 FT
Togal counts	
Single Swing Door 14	14 EA



- FLOOR PLAN KEY NOTES**
- OUTDOOR SHOWER AND EYEWASH
 - CMU SCREEN WALL- SEE ELEVATIONS FOR HEIGHT
 - ELECTRICAL PANELS FLUSH MOUNTED IN 6" STUD WALL
 - GROUND MOUNTED HEAT PUMP UNITS- REFER TO MECHANICAL DRAWINGS
 - OUTDOOR PALLET RACK STORAGE
 - CONCRETE PAD / WALK
 - GROUND MOUNTED CONDENSING UNIT- REFER TO MECHANICAL DRAWINGS
 - WALL MOUNTED EXHAUST FAN- REFER TO MECHANICAL DRAWINGS
 - ELECTRICAL SERVICE- REFER TO ELECTRICAL DRAWINGS
 - LINE OF ROOF OVERHANG
 - SYSTEMS FURNITURE (N.I.C.)
 - DOMESTIC WATER RISER- REFER TO PLUMBING DRAWINGS
 - LOCKERS- REFER TO SPECIFICATIONS
 - FLOOR MOP SINK WITH 20 GAL. WATER HEATER MOUNTED ABOVE- REFER TO PLUMBING DRAWINGS
 - ELECTRIC DRINKING FOUNTAIN
 - IRRIGATION CONTROLLER
 - TELEPHONE MOUNTING BOARD
 - 5' LONG EXHAUST HOOD
 - FIRE SPRINKLER RISER
 - BULLETIN BOARD (SUPPLIED BY OWNER, INSTALLED BY CONTRACTOR)
 - DISHWASHER (SUPPLIED BY OWNER, INSTALLED BY CONTRACTOR)
 - COUNTER MOUNTED EYEWASH
 - 1" SLEEVE THRU WALL FOR FUEL DRAIN @ 30" A.F.F.
 - SECURITY FENCE- 2"Ø SCHEDULE 40 PIPE IN CONCRETE FOOTING, REFER TO DETAIL 9/A-10. CENTER PIPE 1'-0" BACK FROM FACE OF MASONRY WALL

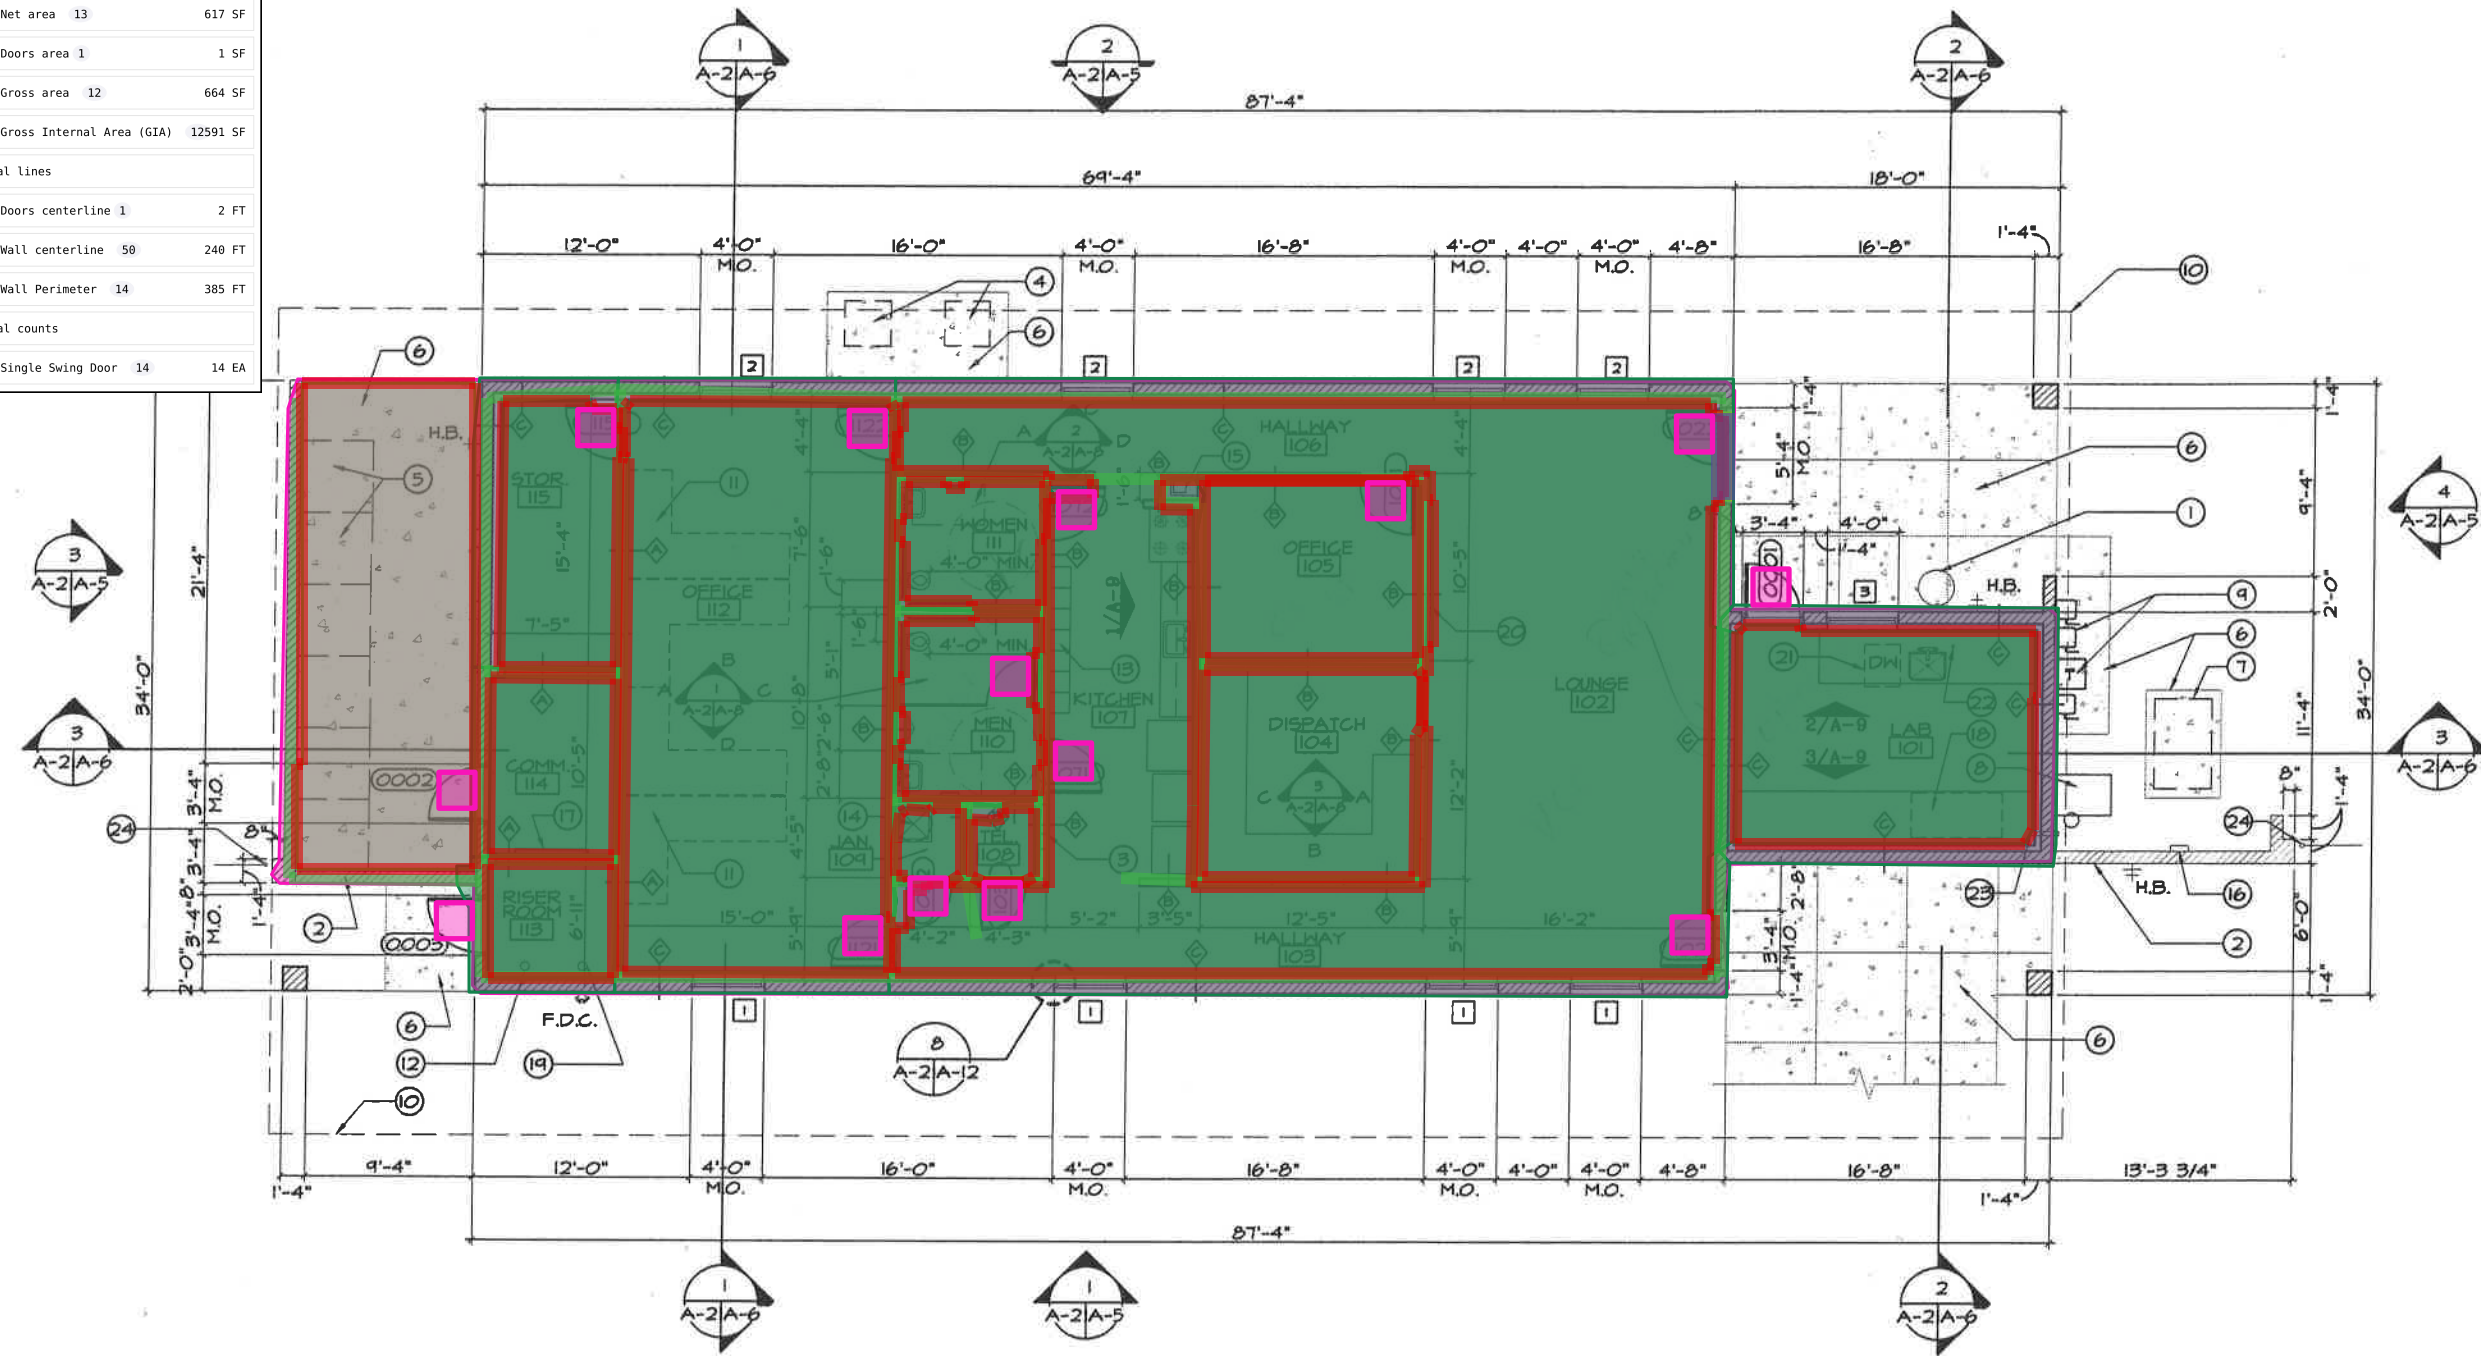


1 FLOOR PLAN

SCALE: 3/16" = 1'-0"

WALL LEGEND		
TYPE	DETAIL	DESCRIPTION
		EXTERIOR 8" CMU WALL
	2/A-II	INTERIOR PARTITION- 5/8" TYPE 'X' GYP. BD. BOTH SIDES 3-5/8" METAL STUD FRAMING, EXTEND TO ROOF STRUCTURE. PROVIDE R-II BATT INSULATION.
	3/A-II	INTERIOR PARTITION- 5/8" TYPE 'X' GYP. BD. BOTH SIDES 3-5/8" METAL STUD FRAMING, EXTEND WALL TO 9'-6" A.F.F.. PROVIDE R-II BATT INSULATION.
	4/A-II	INTERIOR PARTITION- FURR OUT CMU WALL W 5/8" TYPE 'X' GYP. BD. OVER 3-5/8" METAL STUD FRAMING. PROVIDE SPRAY-ON INSULATION. FRAMING AND INSULATION TO EXTEND TO BOTTOM OF ROOF TRUSSES. PROVIDE TYPE W.R. GYP. BD. AT RESTROOM SIDE OF INTERIOR PARTITIONS

DEPARTMENT OF THE NAVY SAN DIEGO		NAVAL FACILITIES ENGINEERING COMMAND SOUTHWEST DIVISION NAVAL FACILITIES CALIFORNIA		SUBMITTED:		SATISFACTORY TO:		DATE		REVISIONS							
				DESIGN:		FAC MANG. OFFICER:		DATE		APPROVED		PREP. BY		DESCRIPTION		SYMBOL	
				DRAWN:		CHECKED:		DATE									
				FP:		DIRECTOR OF ENG.:		DATE									
								SW DW FOR COMMANDER NAVFAC		DATE							
				FLOOR PLAN													
SIZE D IF SHEET IS LESS THAN 22" X 34" IT IS A REDUCED PRINT— SCALE REDUCED ACCORDINGLY		PWO. NO.		PROJECT LOCATION		CONSTR. CONTRACT NO.		SPEC.		NAVFAC DRAWING NO.		SHEET 14 OF		A-2			

Total areas		
	Footprint 1	1,046 SF
	Net area 15	823 SF
	Gross area 12	966 SF
	Gross Internal Area ... 13	893 SF
Total lines		
	Wall centerline 52	334 FT
	Wall Perimeter 15	435 FT

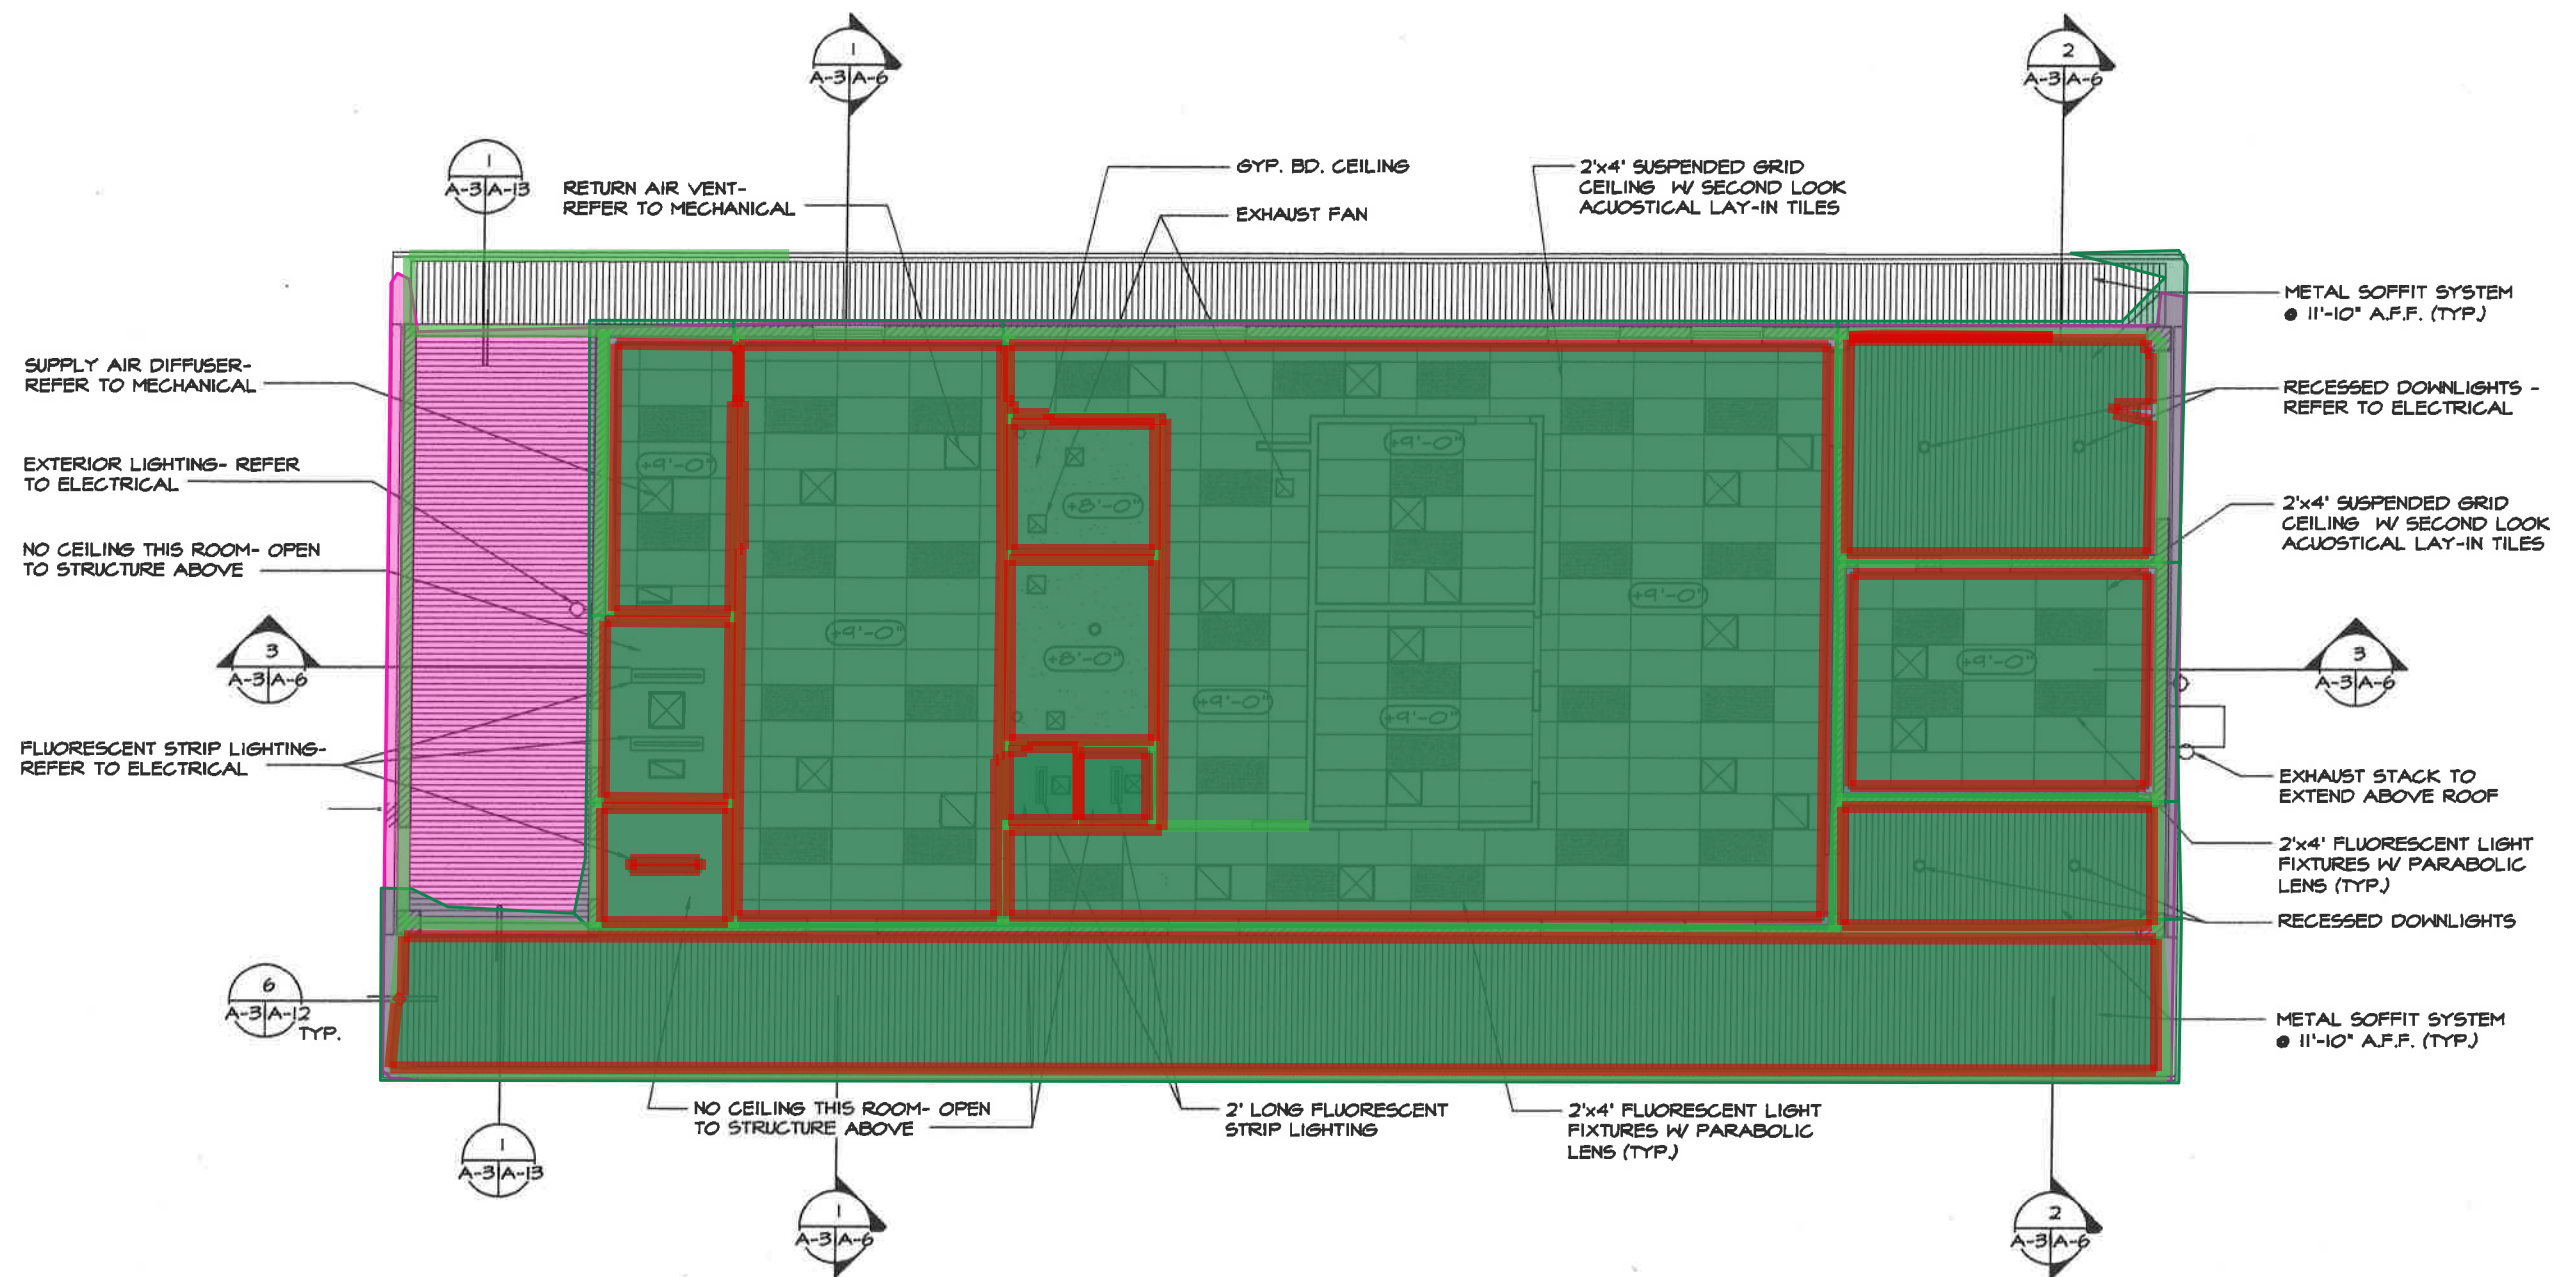

 **1 REFLECTED CEILING PLAN**
SCALE: 3/16" = 1'-0"

DEPARTMENT OF THE NAVY SAN DIEGO		NAVAL FACILITIES ENGINEERING COMMAND SOUTHWEST DIVISION NAVAL FACILITIES CALIFORNIA		SUBMITTED: DESIGN: DRAWING: CHECKED: FP:		SATISFACTORY TO: FAC. MANG. OFFICER: DIRECTOR OF ENG.: SW DIV FOR COMMANDER NAVFAC		DATE DATE DATE DATE		REVISIONS APPROVED DATE PREP. BY DESCRIPTION SYMBOL	
SIZE D IF SHEET IS LESS THAN 22" X 34" IT IS A REDUCED PRINT— SCALE REDUCED ACCORDINGLY				REFLECTED CEILING PLAN							
PWO. NO.											
PROJECT LOCATION											
CONSTR. CONTRACT NO.											
SPEC.											
NAVFAC DRAWING NO.											
SHEET 15 OF											
A-3											