


Total areas		
 Footprint 1	18,648	SF
 Net area 4	16,874	SF
 Gross area 3	8,792	SF
 Gross Internal Area... 2	8,246	SF
Total lines		
 Wall centerline 146	1,157	FT
 Wall Perimeter 10	1,537	FT
Total counts		
 Parking Lot 3	3	EA

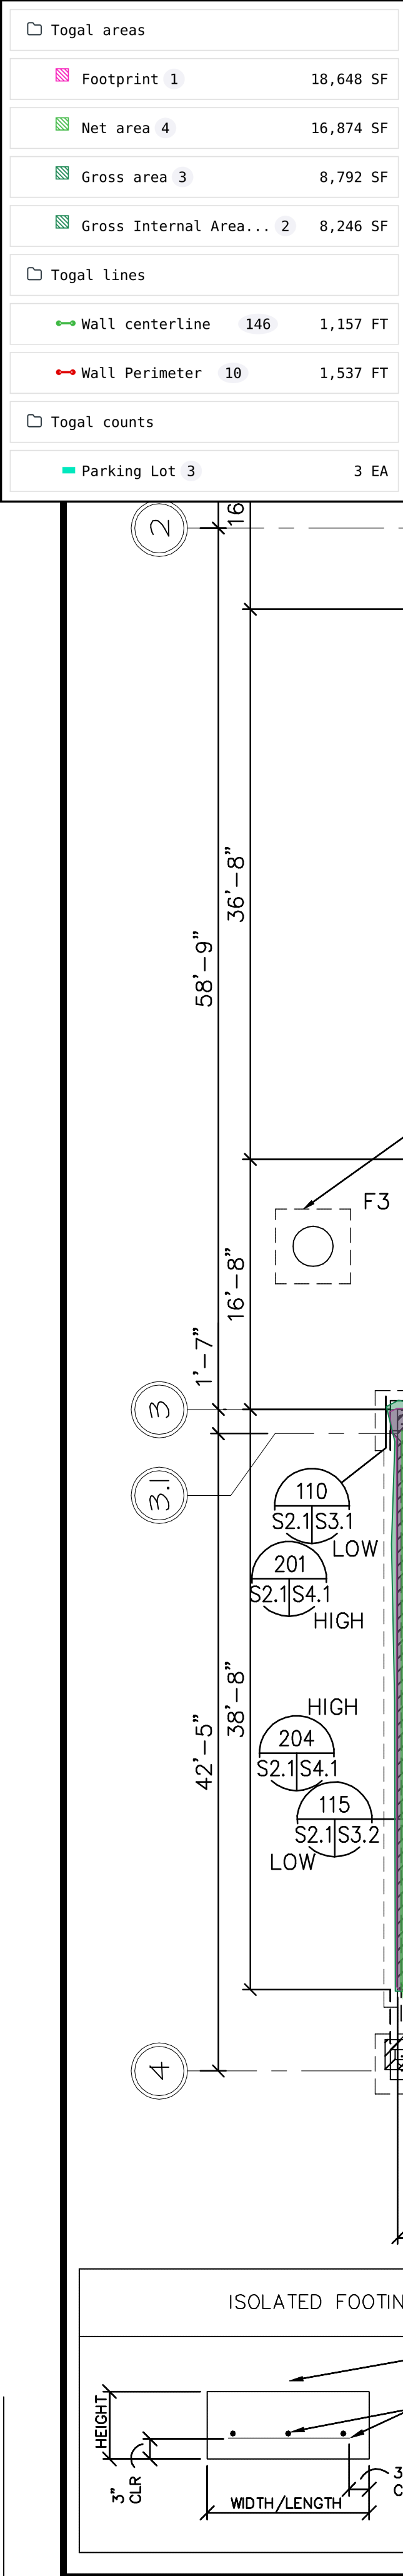

CONTINUOUS FOOTING (WF) SCHEDULE

901-03

FOR CONSTRUCTION ABOVE FOOTING, SEE DETAILS.

LONGITUDINAL REINFORCING. EQUAL SPACING U.N.O.

TRANSVERSE REINFORCING

NOTE: 1. FOR DEPTH OF FOOTING, SEE G.S.N. U.N.O.
 2. CENTER FOOTING ON CONSTRUCTION ABOVE U.N.O.
 3. EXTEND FOOTINGS 12" BEYOND JAMBS U.N.O.

MARK	DIMENSIONS		FOOTING REINFORCING	REMARKS
	HEIGHT	WIDTH		
WF1	12"	3'-0"	4 - #5 CONTINUOUS AND #4 AT 12" O.C. TRANSVERSE	---

SEE S5.3 FOR FOUNDATION PLAN NOTES:

1 - #5 CENTERED IN
SOLID GROUTED CELL
SPACED AT 24" O.C. -
TYPICAL 16'-0" WALL.
ALL WALLS TO BE
SOLID GROUTED.

DEPARTMENT OF THE NAVY SAN DIEGO		NAVAL FACILITIES ENGINEERING COMMAND CALIFORNIA		SUBMITTED:		SATISFACTORY TO:		DATE		APPROVED		DATE		PREP. BY		REVISIONS DESCRIPTION		SYMBOL	
SOUTHWEST DIVISION NAVAL FACILITIES		P-491 YOUTH CENTER MARINE CORPS AIR STATION YUMA, ARIZONA		DESIGN:		FAC MANG. OFFICER:		DATE											
				DRAWN:															
				CHECKED:		DIRECTOR OF ENG.:		DATE											
				DM:															
				AFT LEADER		SW DIV FOR COMMANDER NAVFAC		DATE											
				FP:															
FOUNDATION PLAN																			
SIZE D IF SHEET IS LESS THAN 22" X 34" IT IS A REDUCED PRINT - SCALE REDUCED ACCORDINGLY																			
PWO. NO.																			
PROJECT LOCATION YUMA, ARIZONA																			
CONSTR. CONTRACT NO. N68711-02-C-2018																			
SPEC.																			
NAVFAC DRAWING NO. 8175782																			
SHEET 49 OF																			
S2.1																			